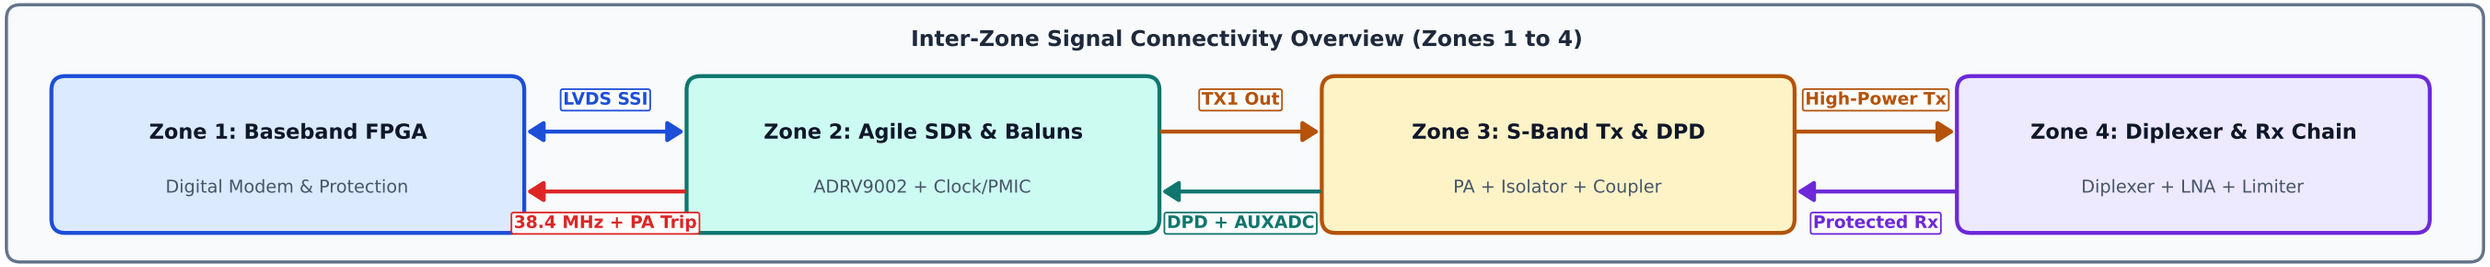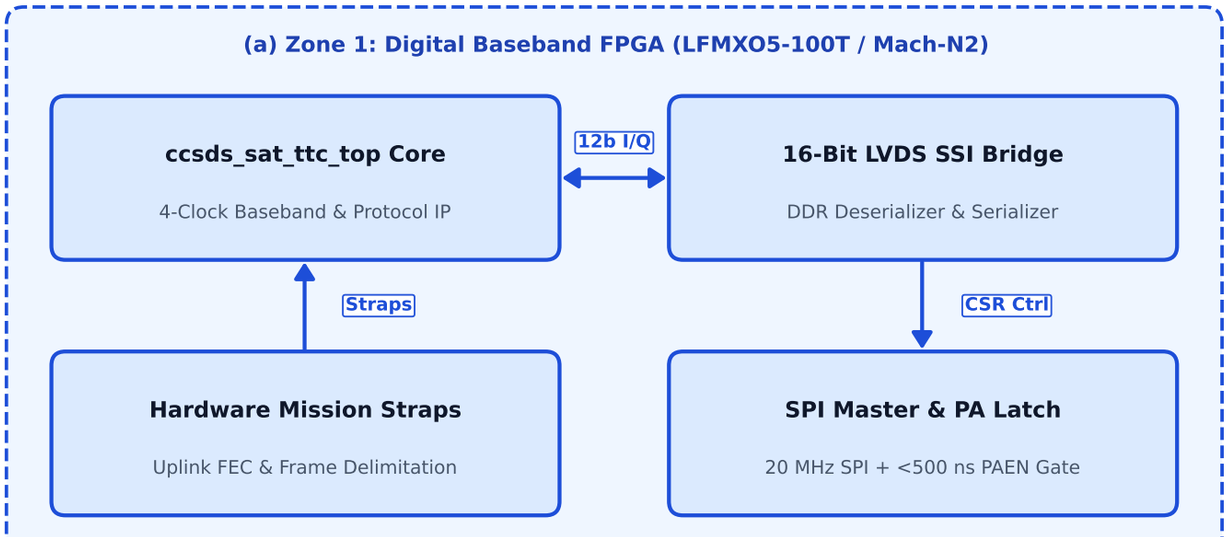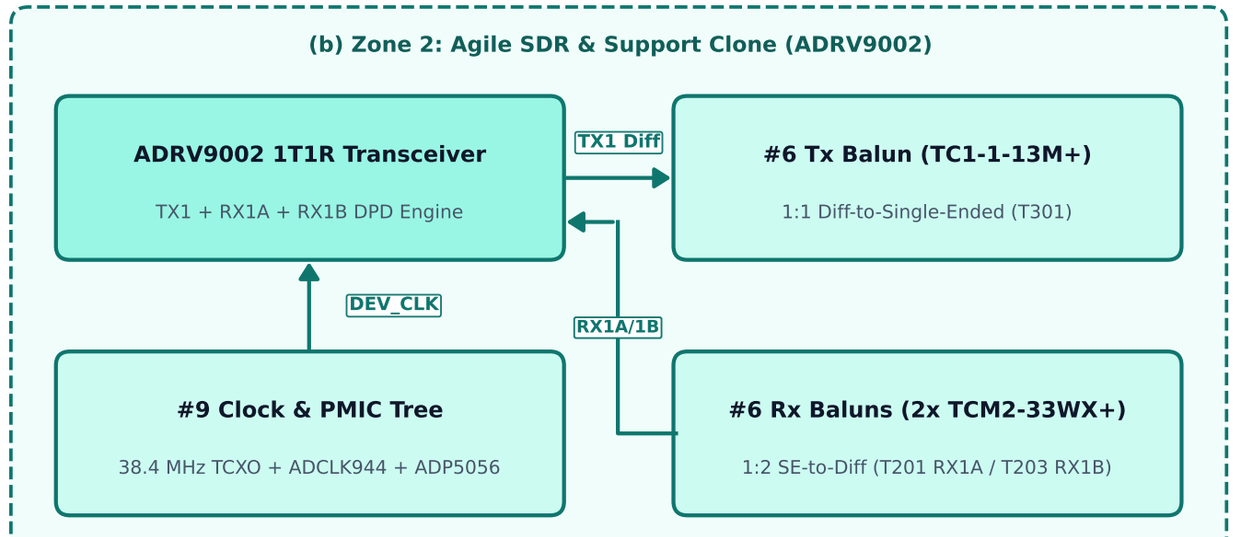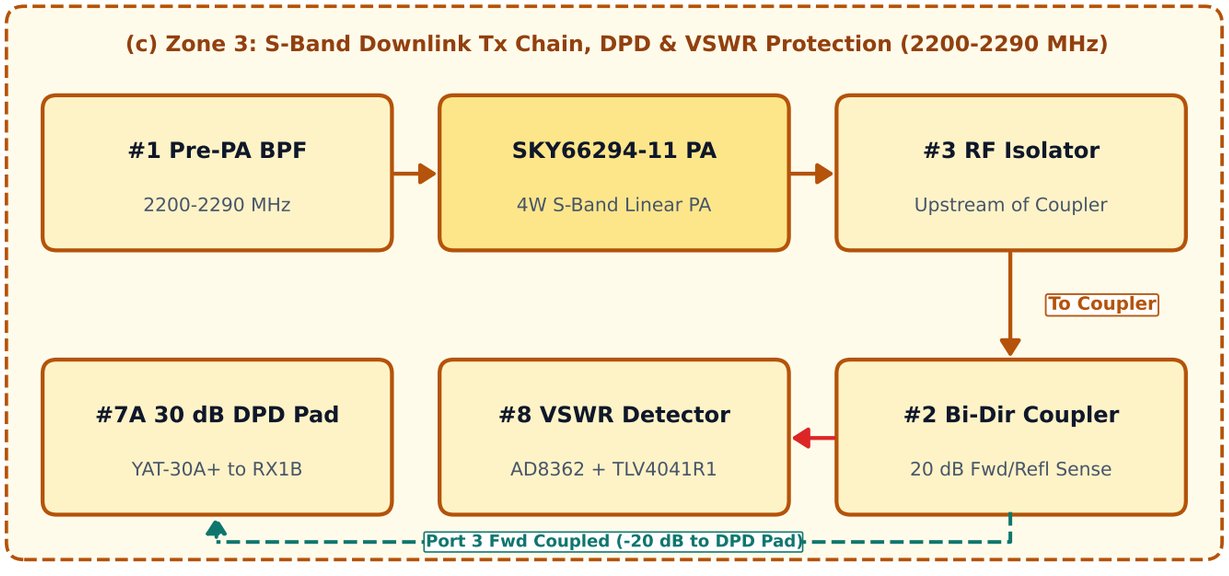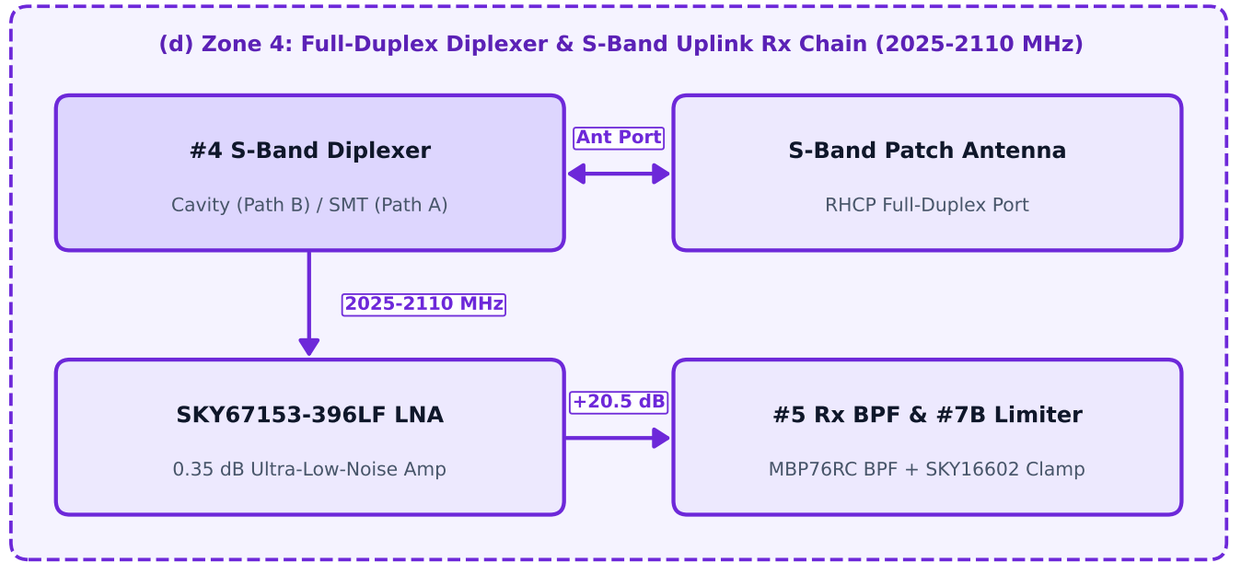# S-Band Full-Duplex Transceiver Schematic Architecture: Inter-Zone Overview & Focused Zone Sub-Diagrams